Plano PPS- 2018

CERTIFICO: que la presente copia de plano es aparentemente igual a su original que se encuentra archivado con el número **995** al Registro de Propiedad del año **2018** a mi cargo. Valdivia, 10 de marzo de 2023.-

0995-18AP-230310-IG
Documento incorpora firma electrónica avanzada
consulte validez en www.cbrchile.cl

Teodoro Croquevielle Brand
Conservador - Archivero
Valdivia

Firmado digitalmente por TEODORO ARMANDO CROQUEVIELLE BRAND
Nombre de reconocimiento (DN): c=CL, st=LOS RÍOS, l=VALDIVIA, o=TEODORO CROQUEVIELLE BRAND, ou=CONSERVADOR Y ARCHIVERO JUDICIAL Titular 1024, cn=TEODORO ARMANDO CROQUEVIELLE BRAND, email=CBR@CBRVALDIVIA.CL
Fecha: 2023.03.13 08:02:36 -03'00'

PLANO DE SUBDIVISION PREDIOS RUSTICOS
Lote A-1-1

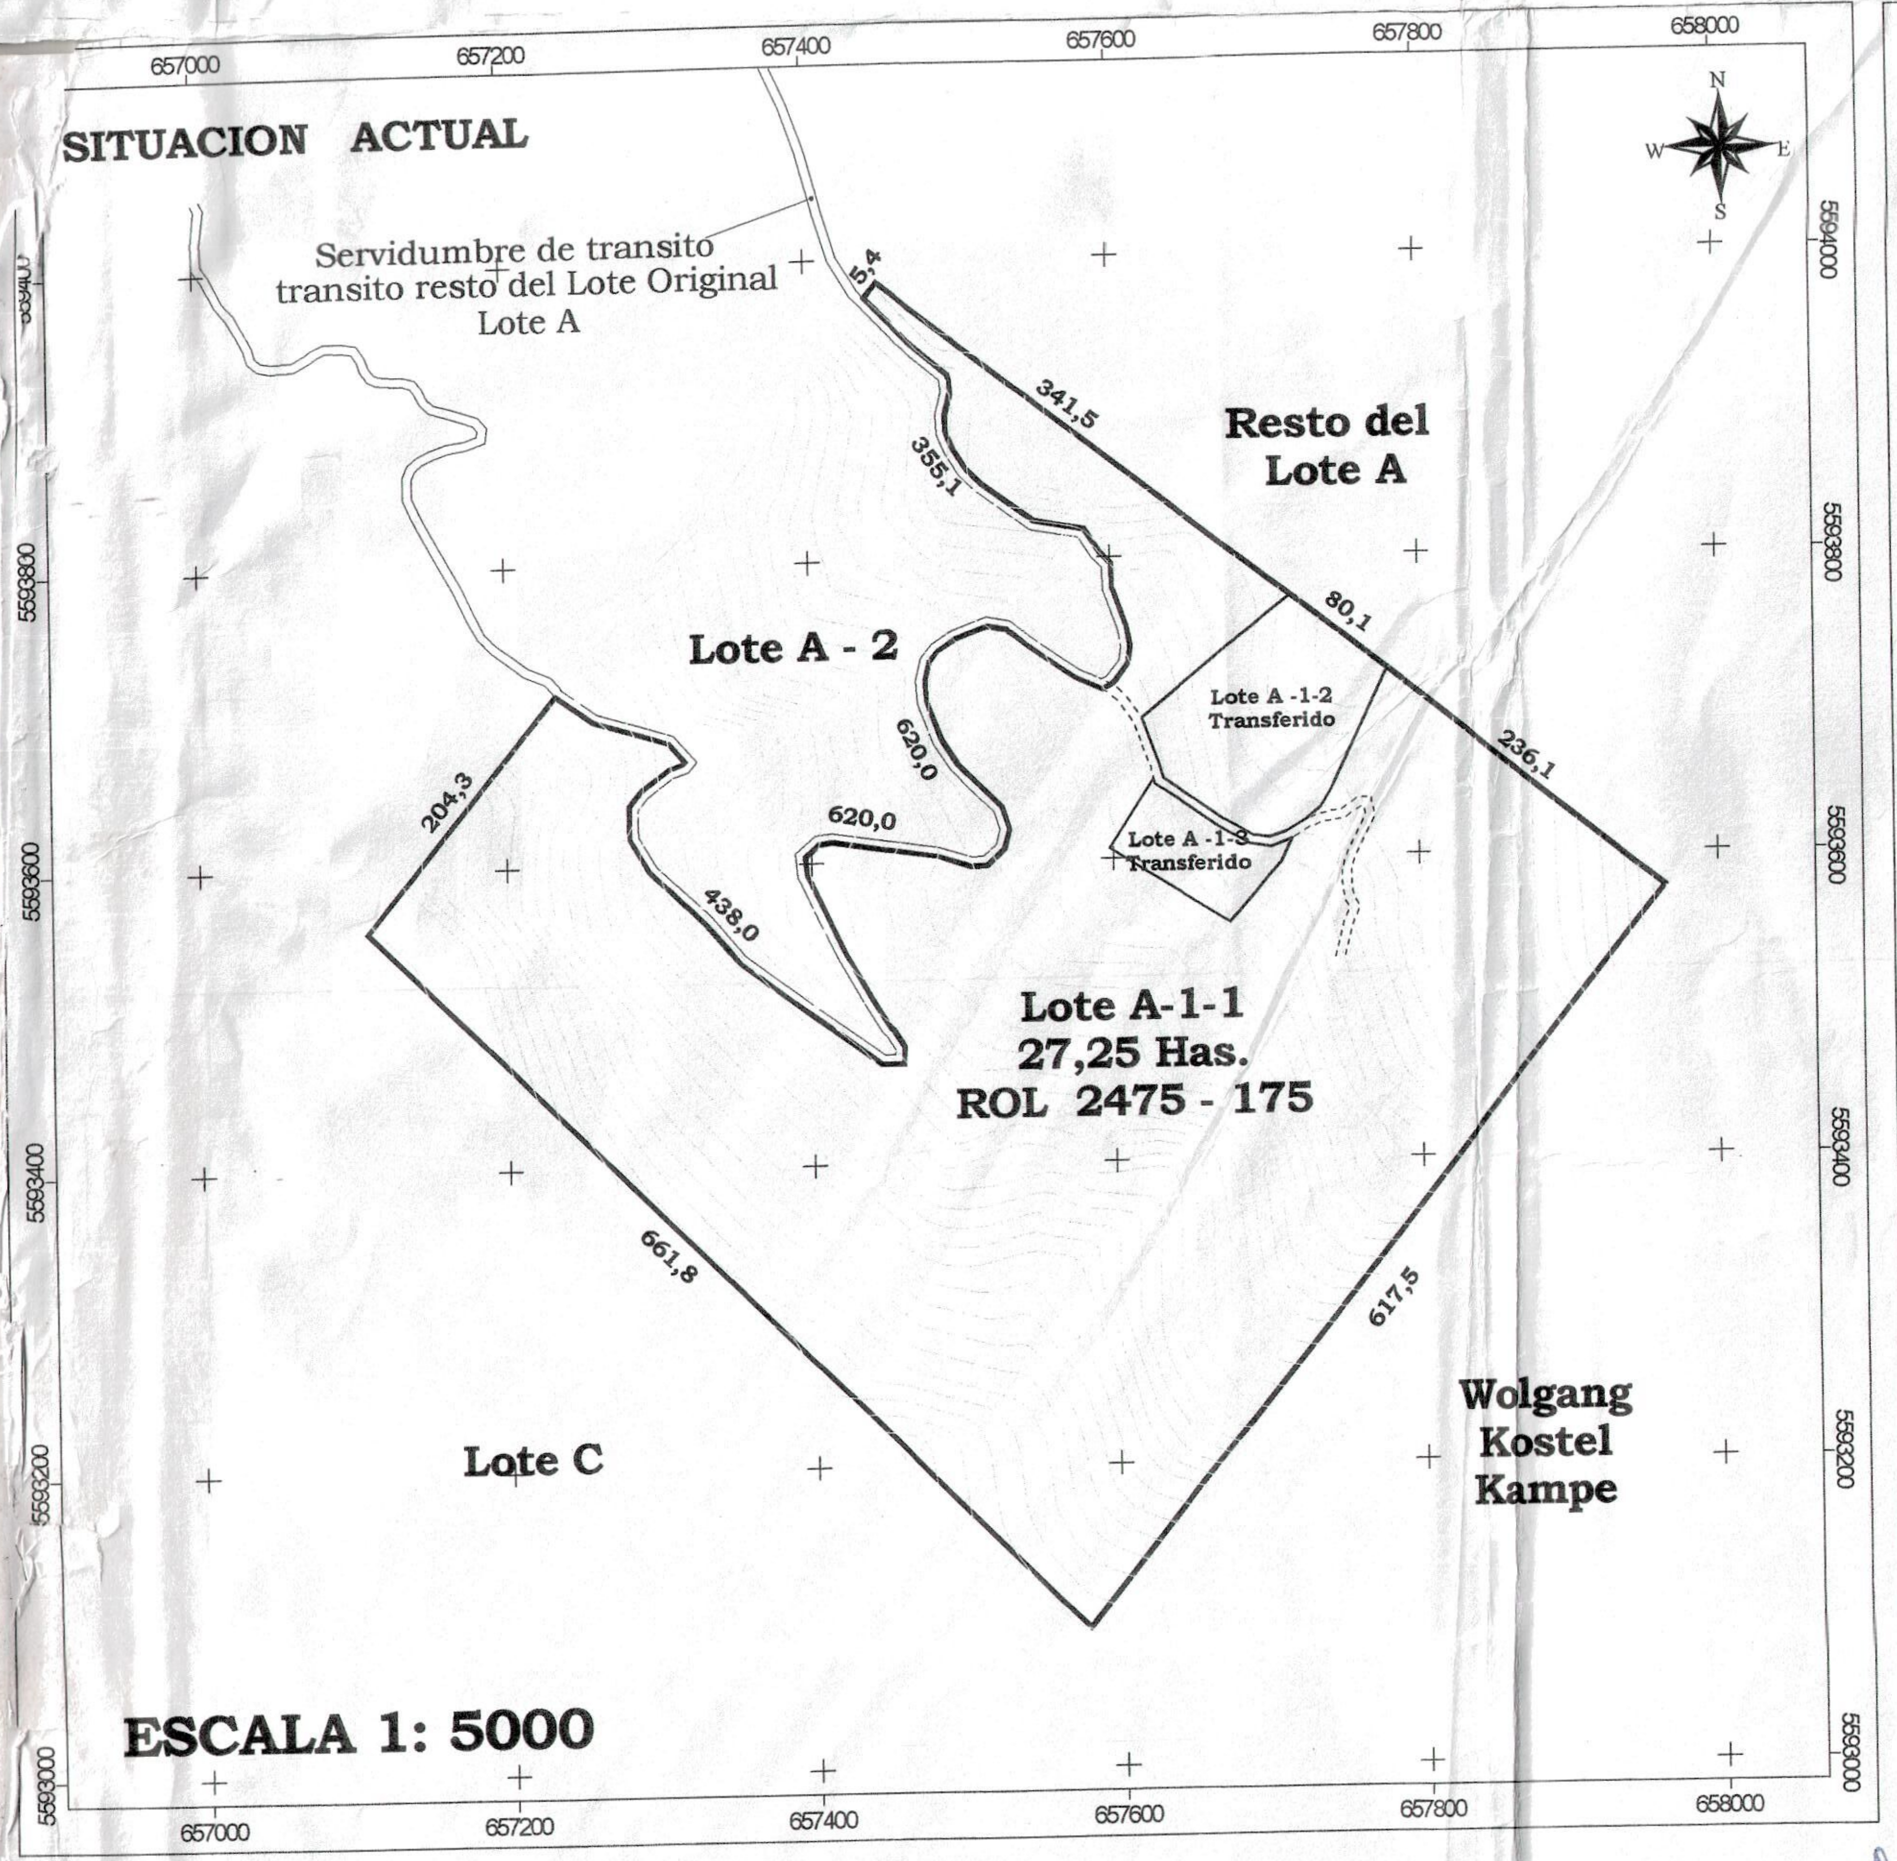

ESCALA 1: 5000

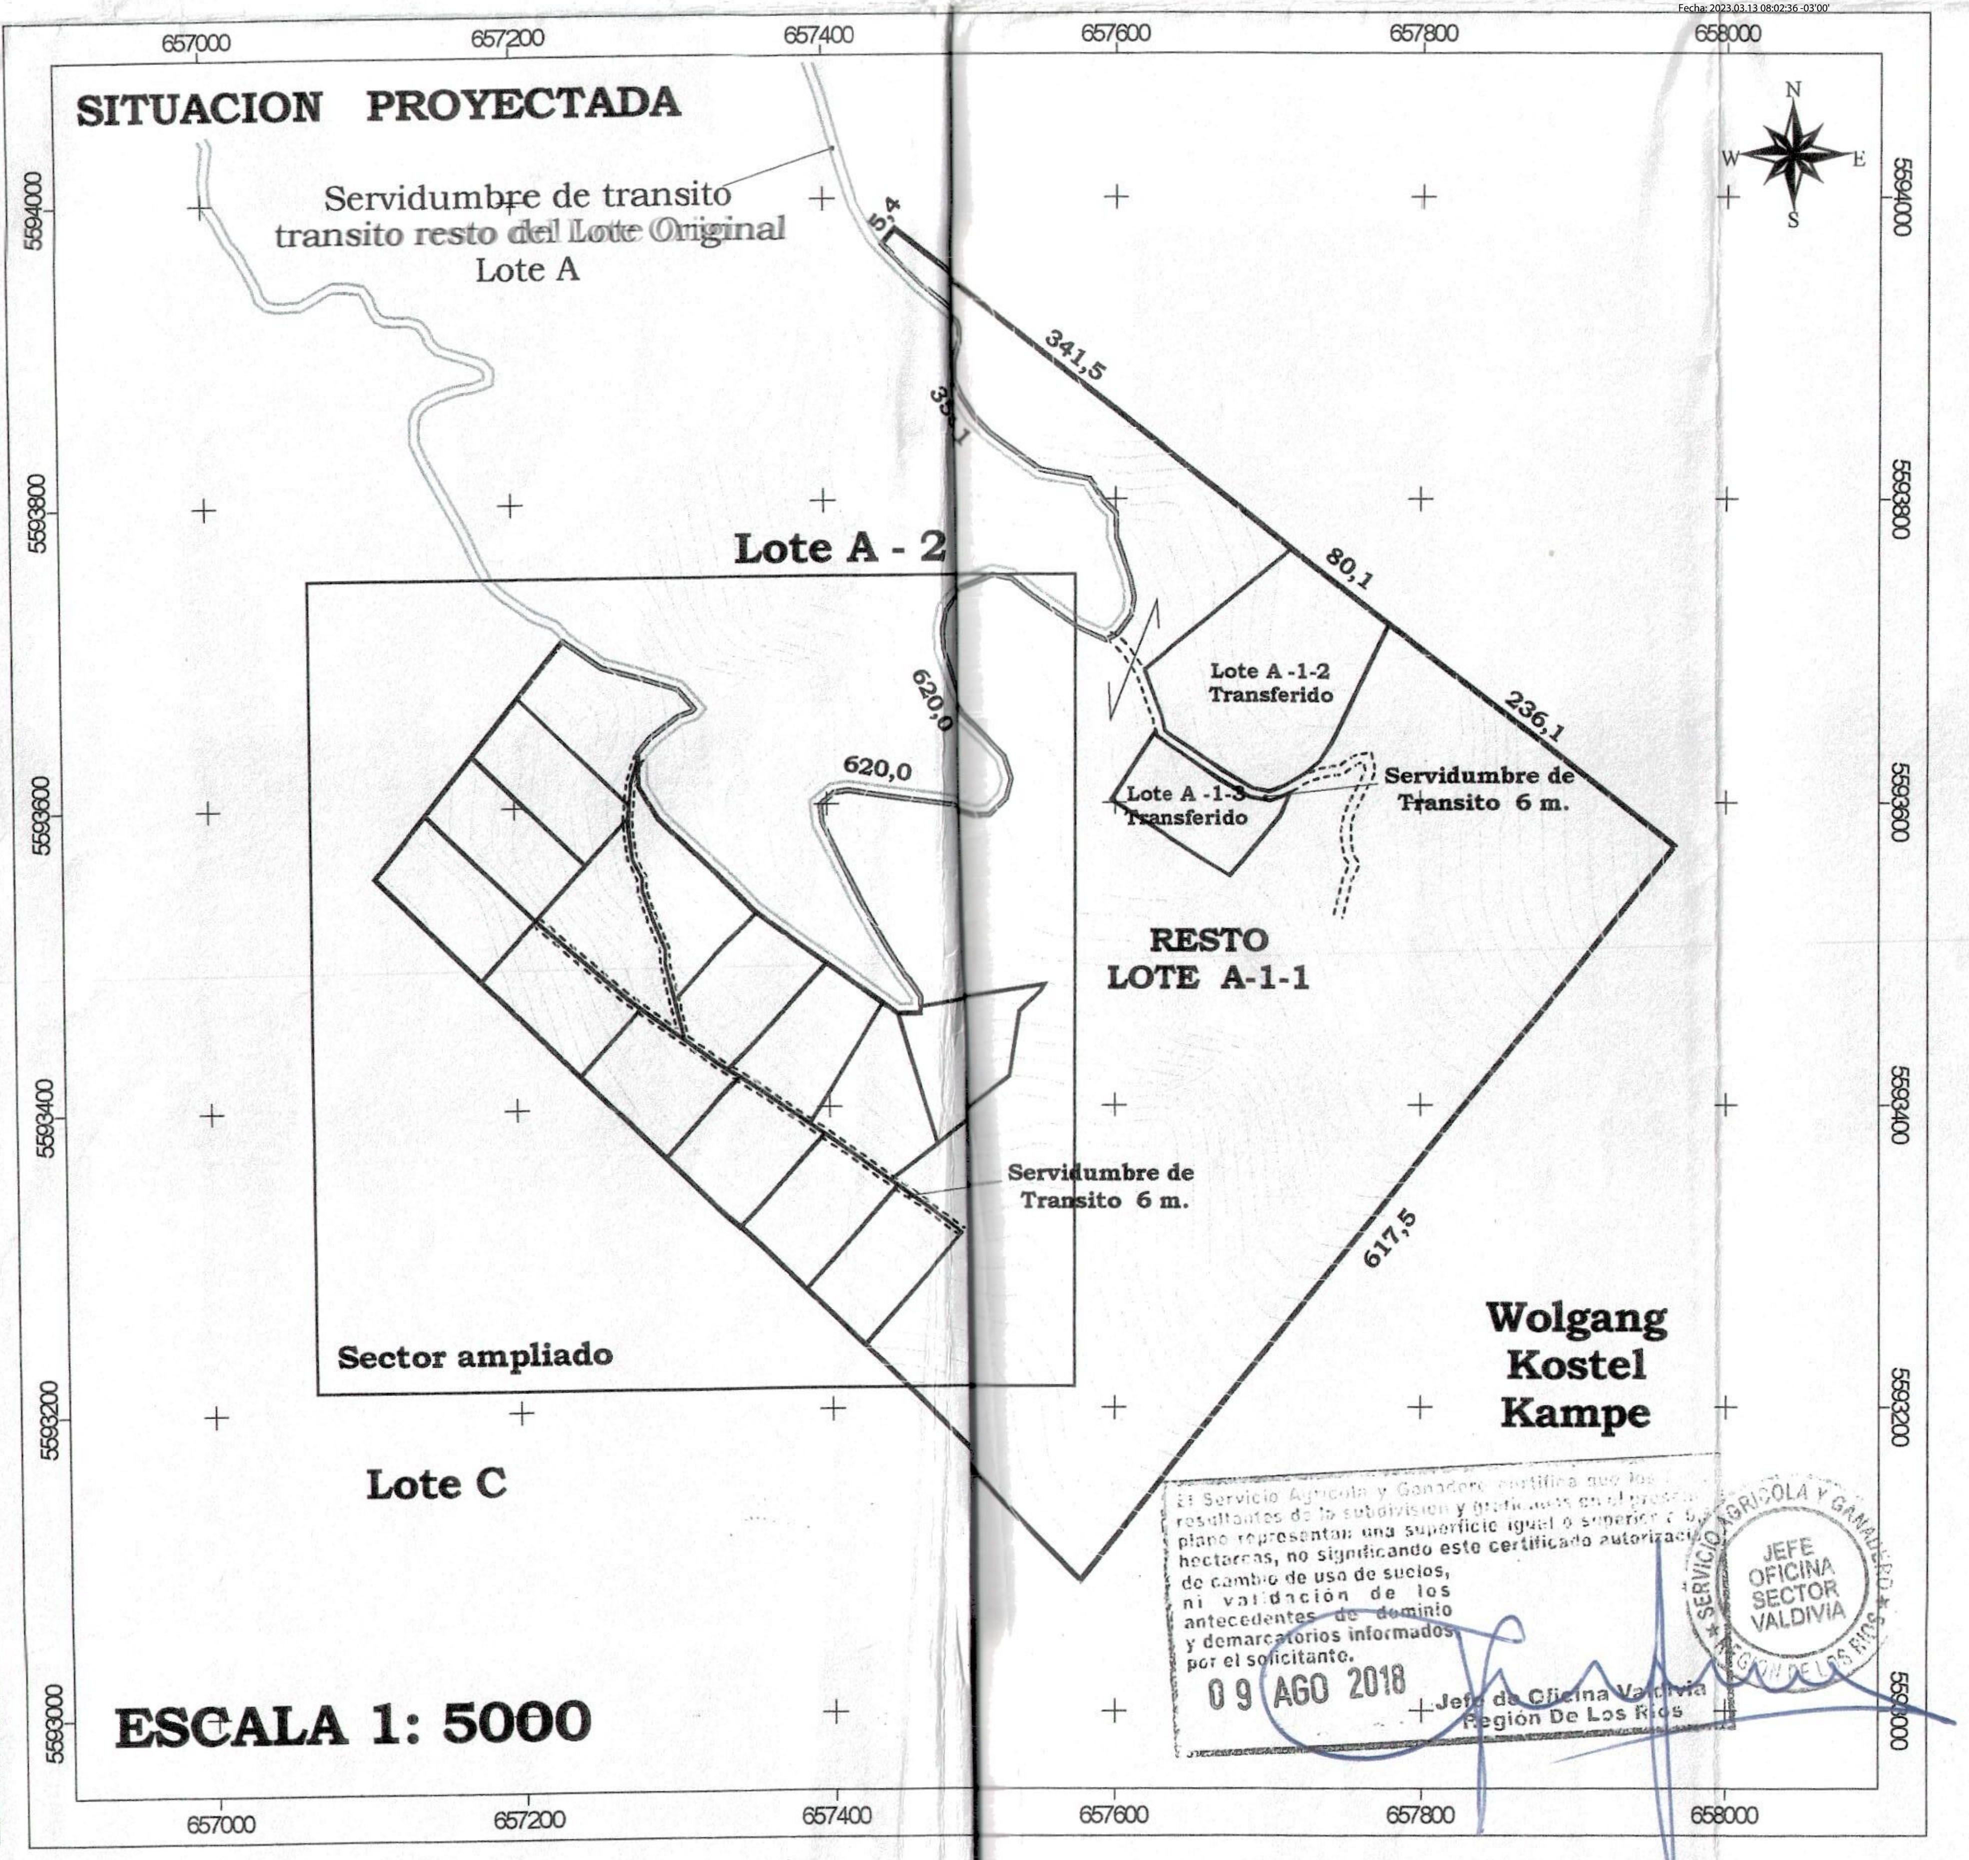

El Servicio Agrícola y Ganadero certifica que los resultantes de la subdivisión y graficados en el presente plano representan una superficie igual o superior a 0,5 hectáreas, no significando este certificado autorización de cambio de uso de suelos, ni validación de los antecedentes de dominio y demarcatorios informados por el solicitante.

09 AGO 2018

Jefe de Oficina Valdivia
Región De Los Ríos

JEFE OFICINA SECTOR VALDIVIA

ESCALA 1: 5000

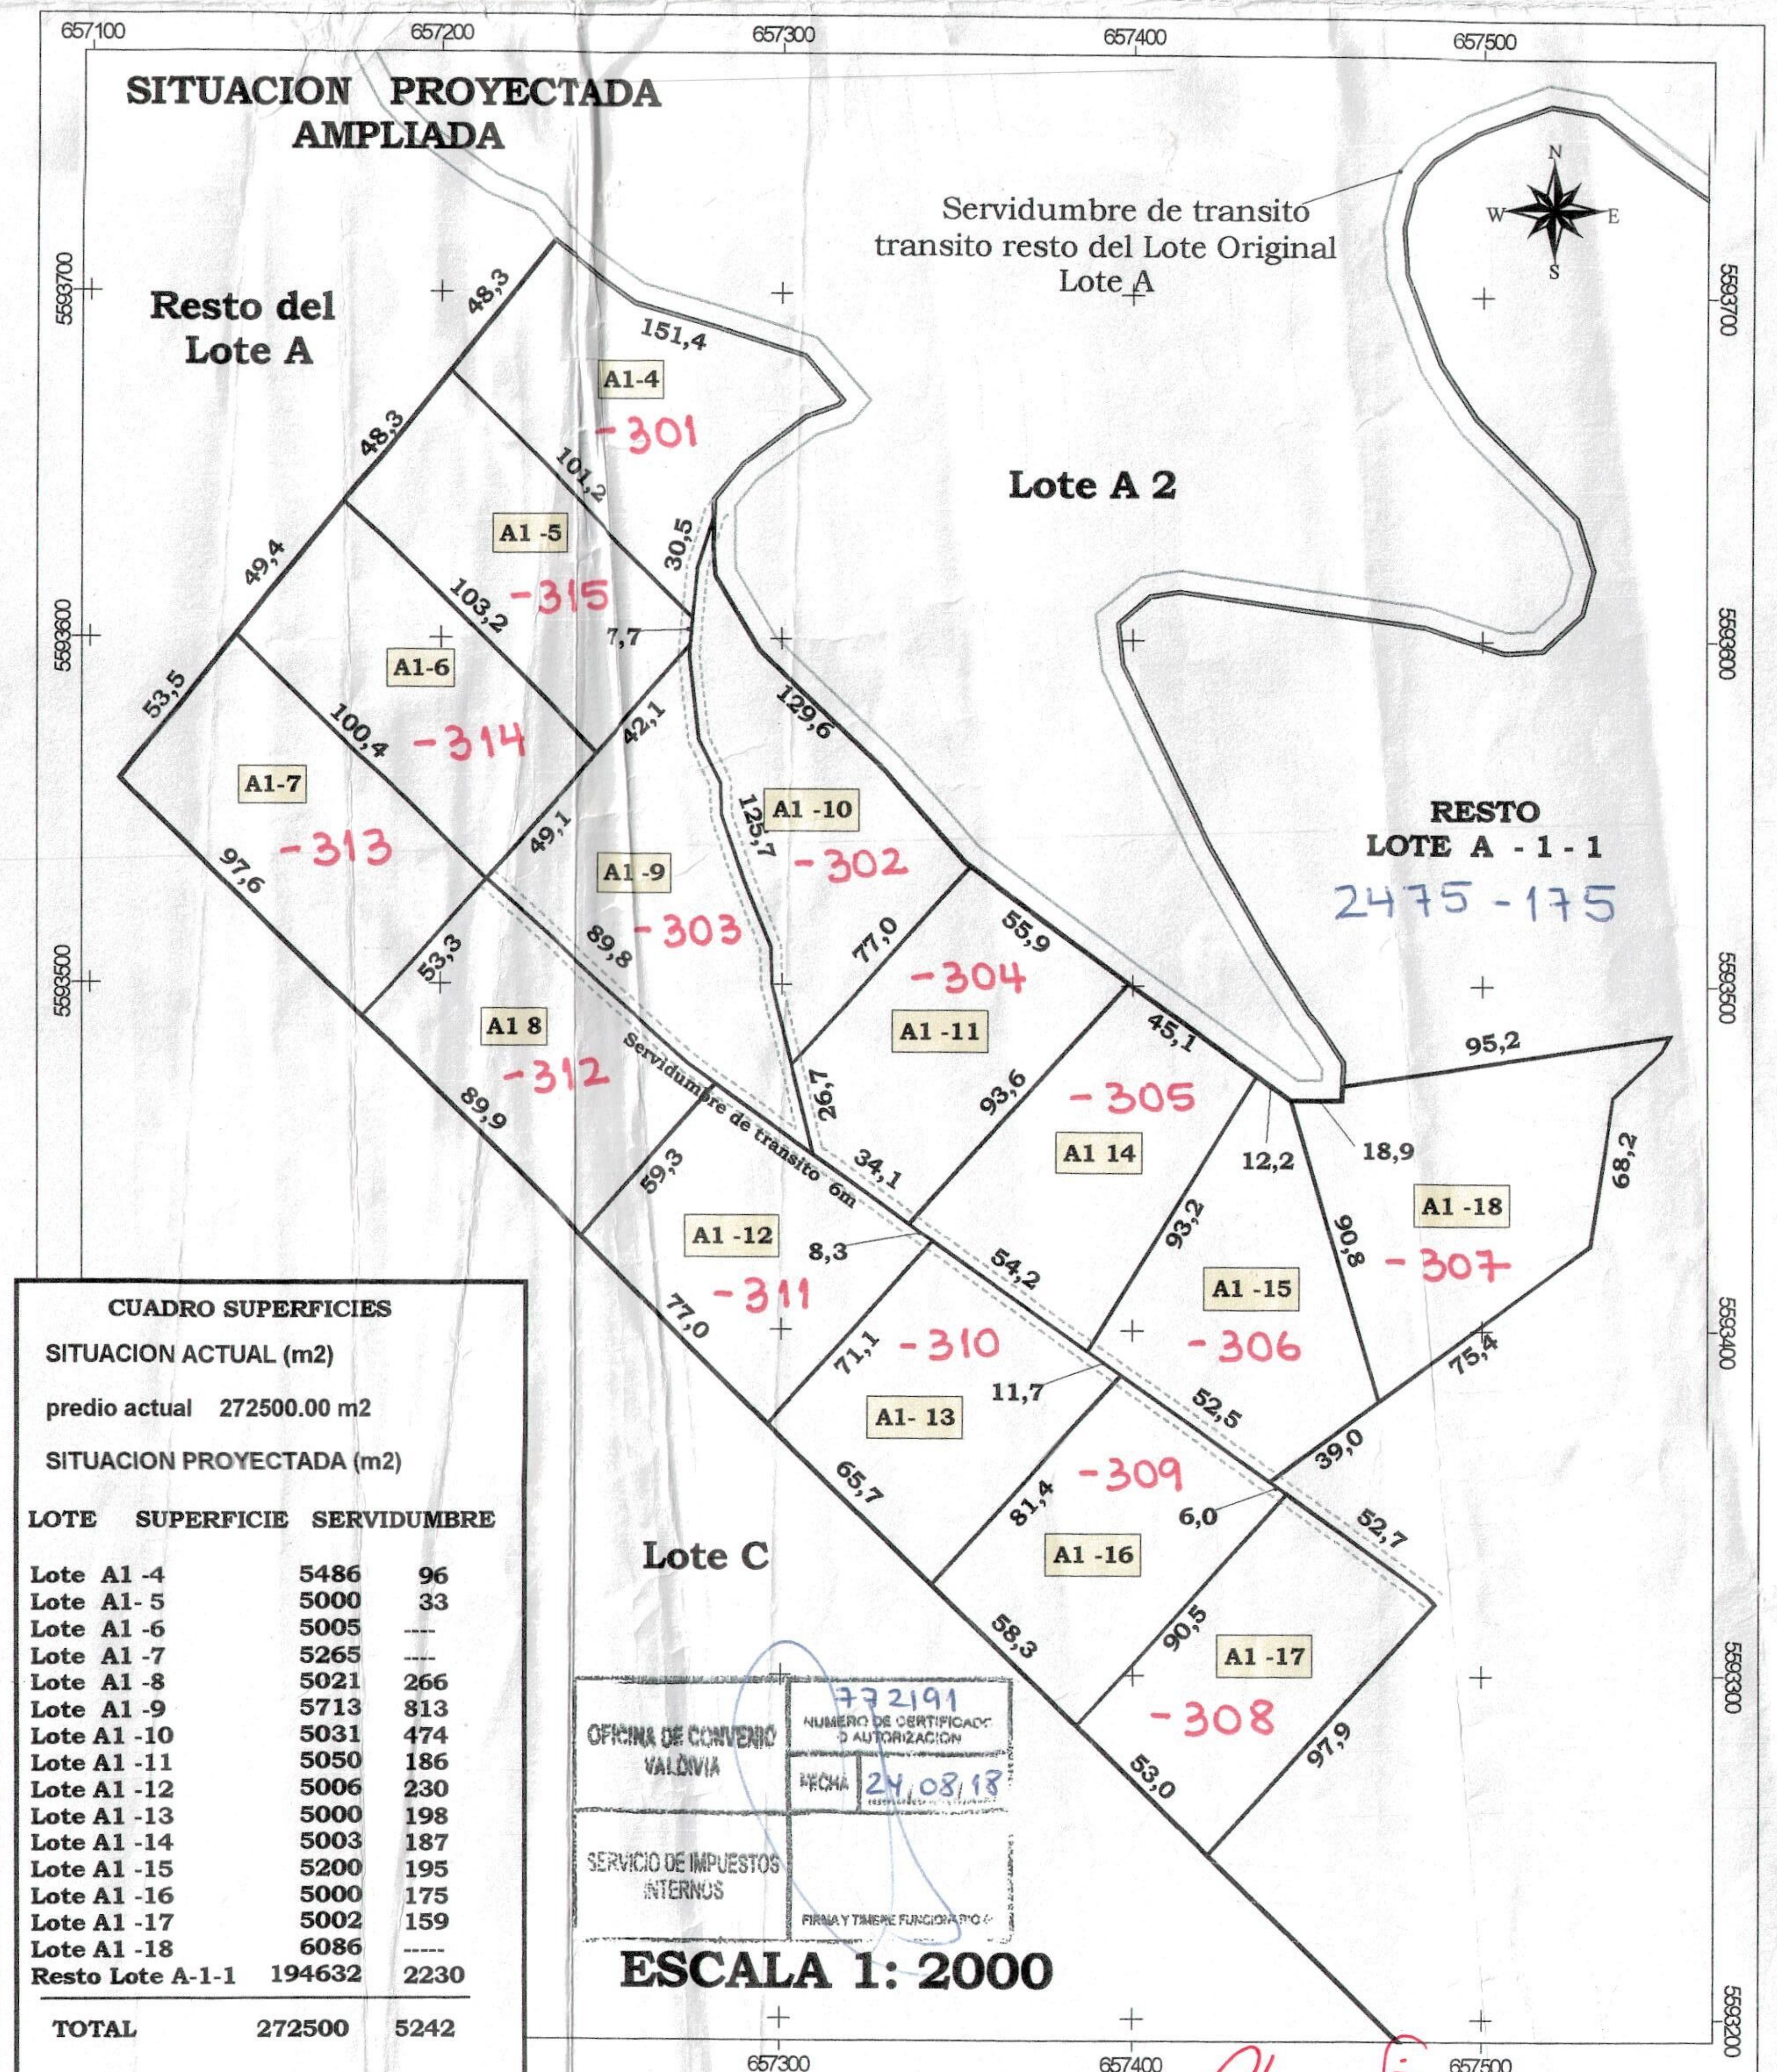

CUADRO SUPERFICIES

SITUACION ACTUAL (m2)

predio actual 272500.00 m2

SITUACION PROYECTADA (m2)

LOTE	SUPERFICIE	SERVIDUMBRE
Lote A1 -4	5486	96
Lote A1- 5	5000	33
Lote A1 -6	5005	----
Lote A1 -7	5265	----
Lote A1 -8	5021	266
Lote A1 -9	5713	813
Lote A1 -10	5031	474
Lote A1 -11	5050	186
Lote A1 -12	5006	230
Lote A1 -13	5000	198
Lote A1 -14	5003	187
Lote A1 -15	5200	195
Lote A1 -16	5000	175
Lote A1 -17	5002	159
Lote A1 -18	6086	-----
Resto Lote A-1-1	194632	2230
TOTAL	272500	5242

OFICINA DE CONVENIO VALDIVIA	772191 NUMERO DE CERTIFICADO O AUTORIZACION FECHA 24,08,18
SERVICIO DE IMPUESTOS INTERNOS	FIRMA Y TIMBRE FUNCIONARIO

ESCALA 1: 2000

UBICACION

Región	:	De Los Rios
Provincia	:	Valdivia
Comuna	:	Valdivia
Lugar	:	Quitacalzon
Superficie	:	27,25 Has.
Rol S.I.I.	:	2475 - 175

SIMBOLOGÍA

▬	Límite Predio
—	Lotes
〰	Cursos de agua
-------	Servidumbre
〰	Curva de nivel
20	Cotas (m)

Propiedad inscrita a fojas 3278 Vta. Nº 3527 . del año 2014, registro de propiedad del conservador de B.R. Valdivia

Datum WGS 84 Huso 18 Sur

PROPIETARIO

Sergio Alejandro Becerra Brun
RUT : 8.398.608 - 5

PROFESIONAL

Pablo Latino Wunderlich
RUT: 8.911.650 - 3
Arquitecto

Control Terreno: Jose Miguel Fiero Arias

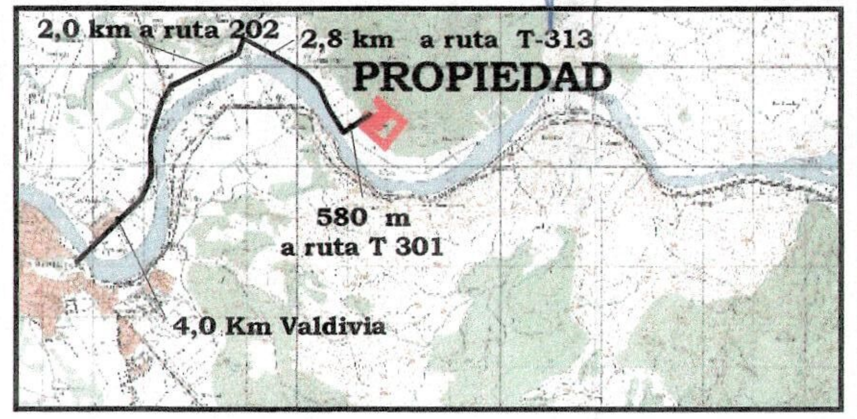

Plano N° 995-2018.-